


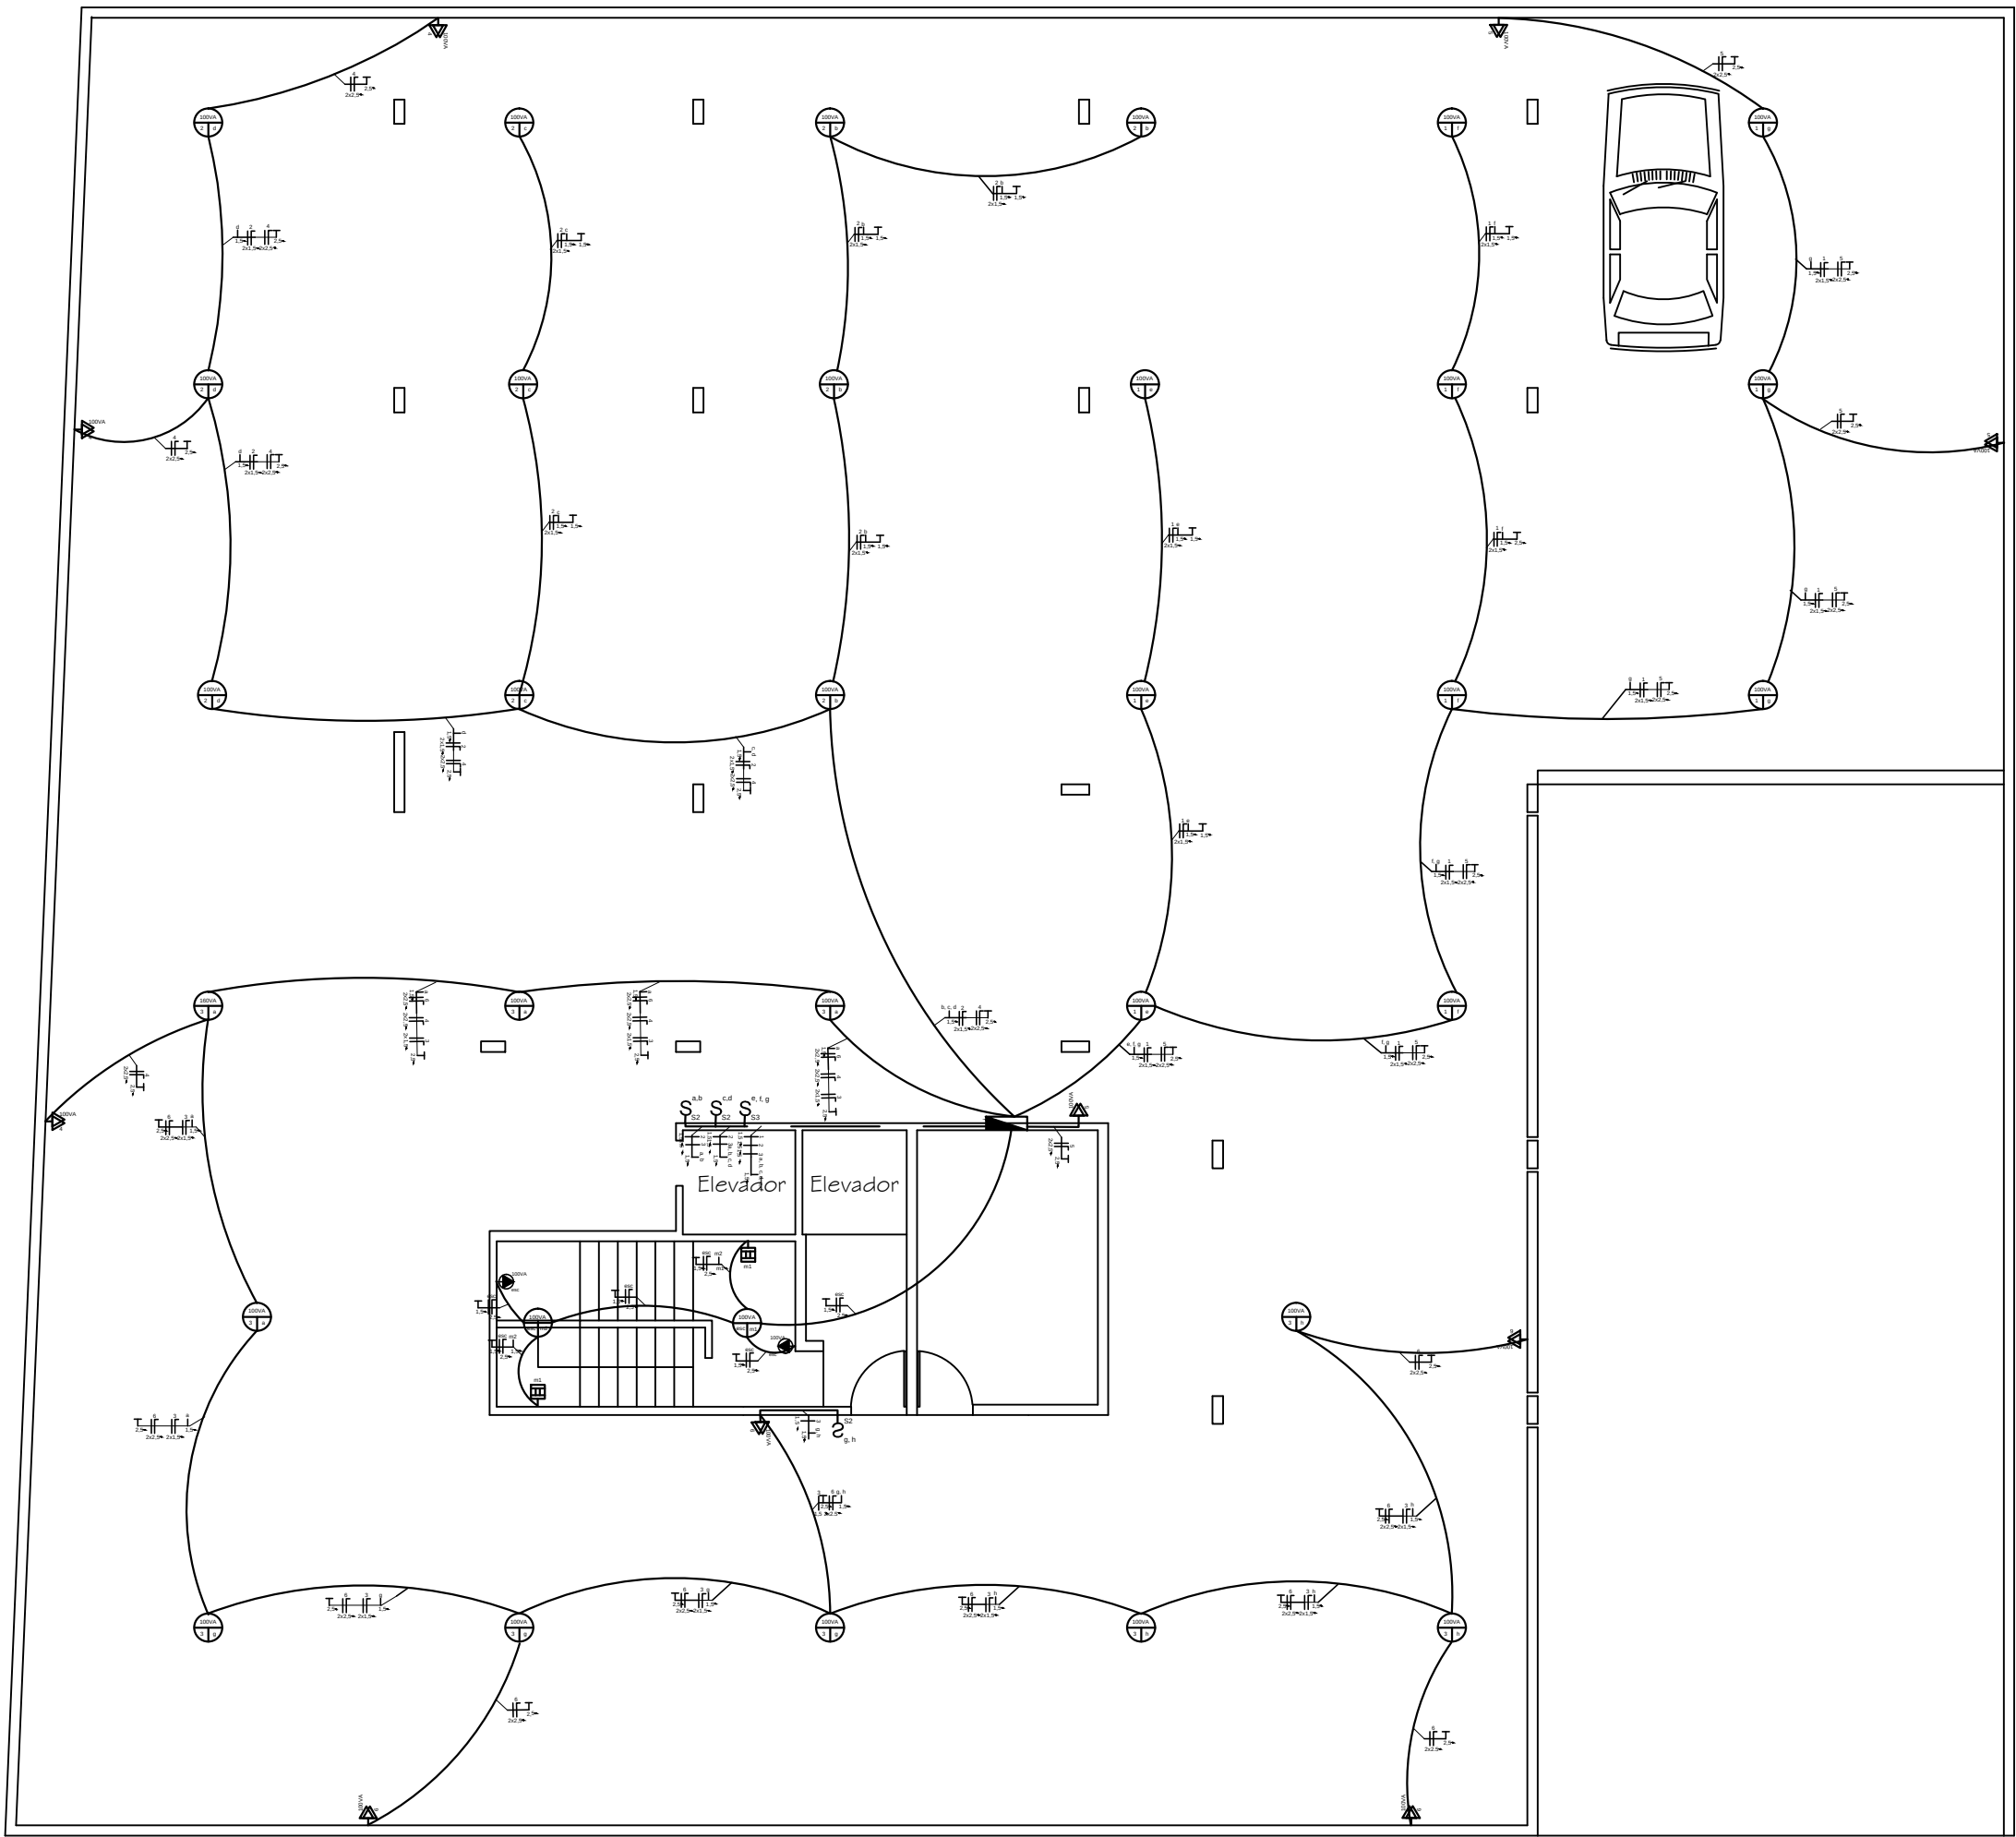

PLANTA DE SUBSOLO
Escala _____ 1/50

QDG - Garagem							
	CIRCUITO	POTÊNCIA	TENSÃO	CORRENTE	FASE	CONDUTOR	PE
	01	1000 VA	220 V	4,55 A	A	2x1,5 mm²	1,5 mm²
	02	1000 VA	220 V	4,55 A	B	2x1,5 mm²	1,5 mm²
	03	1000 VA	220 V	4,55 A	C	2x1,5 mm²	1,5 mm²
	04	300 VA	220 V	1,37 A	A	2x2,5 mm²	2,5 mm²
	05	300 VA	220 V	1,37 A	B	2x2,5 mm²	2,5 mm²
	06	400 VA	220 V	1,82 A	C	2x2,5 mm²	2,5 mm²
	07	7360 VA	220 V	33,46 A	ABC	7x4 mm²	4 mm²
RESERVA CIRCUITAL (NBR 5410) : 3 CIRCUITOS							

Legenda Técnica			
	Ponto de Luz Incandescente		Ponto de Luz Fluorescente de Parede
	Tomada de uso geral - baixa - dupla		Interrupor. Tipos: S1 - Simples; S2 - duplo; S3 - Triplo; 3W - Three Way
	Tomada de uso geral - média - dupla		Sensor de Presença
	Tomada de uso geral - alta - dupla		Caixa de Distribuição
	Tomada de uso específico - baixa - simples		Representação de mm²
	Tomada de uso específico - média - simples		Eletroduto Teto
	Tomada de uso específico - alta - simples		Eletroduto Parede
	Representação dos fios que passam em cada eletroduto. Respectivamente fase, neutro, terra e retorno		Eletroduto Solo

PROJETO DE INSTALAÇÕES ELÉTRICAS UFRN - 2015.1			
CLIENTE:		José Luiz da Silva Júnior	
OBRA:		Projeto de um Edifício Residencial	
Detalhamento do Projeto Elétrico da Garagem			
PROJETISTAS: Frankelene Pinheiro/ Lucas Marcelino/ Pedro Yochinori		DESENHISTA: Lucas Marcelino	Prancha: 03/04
ESCALA: 1:50	DATA: 03/06/2015	ARQUIVO: Planta_Garagem.dwg	