
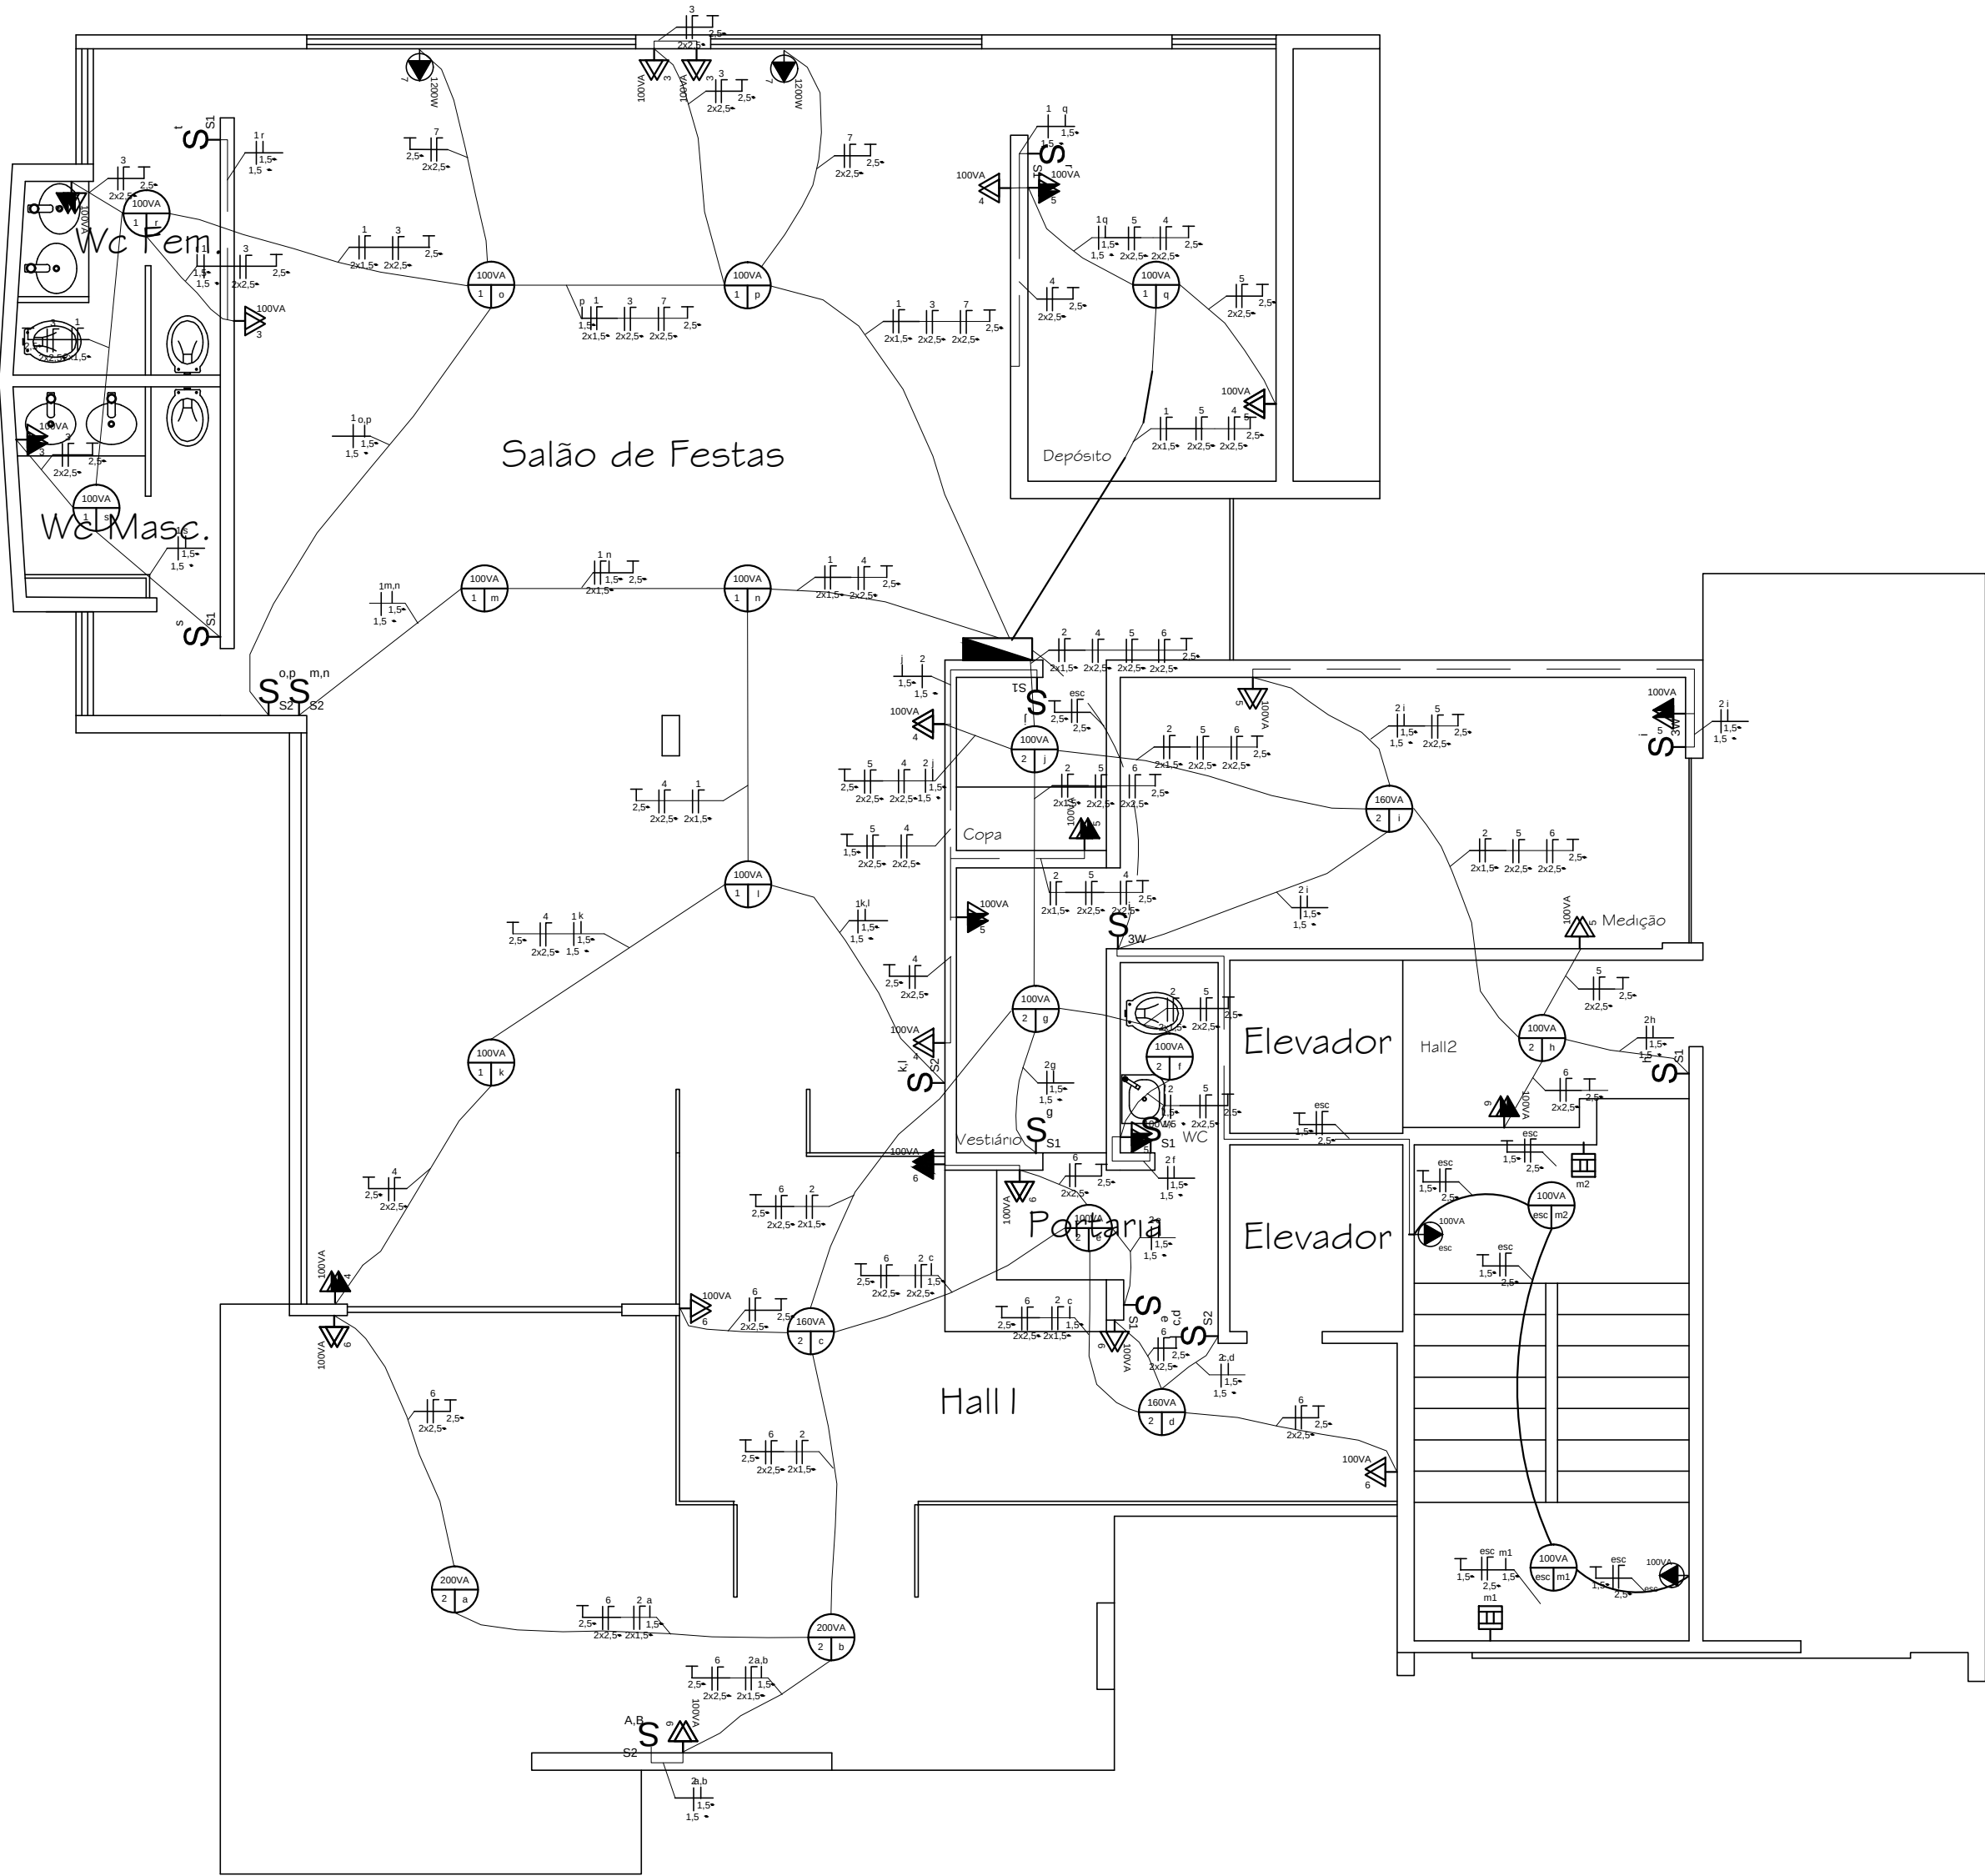


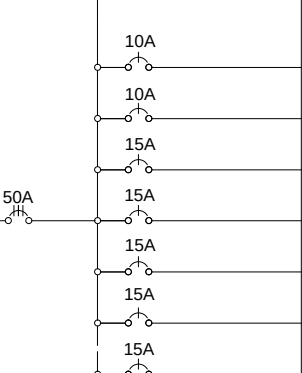

QDG - Térreo								
A B C		CIRCUITO	POTÊNCIA	TENSÃO	CORRENTE	FASE	CONDUTOR	PE
		01	1300 VA	220 V	5,91 A	A	2x1,5 mm ²	1,5 mm ²
		02	1220 VA	220 V	5,54 A	B	2x1,5 mm ²	1,5 mm ²
		03	500 VA	220 V	2,27 A	A	2x2,5 mm ²	2,5 mm ²
		04	500 VA	220 V	2,27 A	B	2x2,5 mm ²	2,5 mm ²
		05	800 VA	220 V	3,64 A	B	2x2,5 mm ²	2,5 mm ²
		06	720 VA	220 V	3,27 A	A	2x2,5 mm ²	2,5 mm ²
		07	2400 W	220 V	10,91 A	C	2x2,5 mm ²	2,5 mm ²
		RESERVA CIRCUITAL (NBR 5410) : 3 CIRCUITOS						

Legenda Técnica			
	Ponto de Luz Incandescente		Ponto de Luz Fluorescente de Parede
	Tomada de uso geral - baixa - dupla		Interrupor. Tipos: S1 - Simples; S2 - duplo; S3 - Triplo; 3W - Three Way
	Tomada de uso geral - média - dupla		Sensor de Presença
	Tomada de uso geral - alta - dupla		Caixa de Distribuição
	Tomada de uso específico - baixa - simples		Representação de mm ²
	Tomada de uso específico - média - simples		Eletroduto Teto
	Tomada de uso específico - alta - simples		Eletroduto Parede
	Representação dos fios que passam em cada eletroduto. Respetivamente fase, neutro, terra e retorno		Eletroduto Solo

PLANTA BAIXA - PAVTO. TÉRREO

Escala _____ 1/50

PROJETO DE INSTALAÇÕES ELÉTRICAS			
UFRN - 2015.1			
CLIENTE:			
José Luiz da Silva Júnior			
OBRA:			
Projeto de um Edifício Residencial			
Detalhamento do Projeto Elétrico do Térreo			
PROJETISTAS:		Frankelene Pinheiro/ Lucas Marcelino/ Pedro Yochinori	DESENHISTA: Frankelene Pinheiro
ESCALA:	DATA:	ARQUIVO:	02/04
1:50	03/06/2015	Planta_Térreo.dwg	