

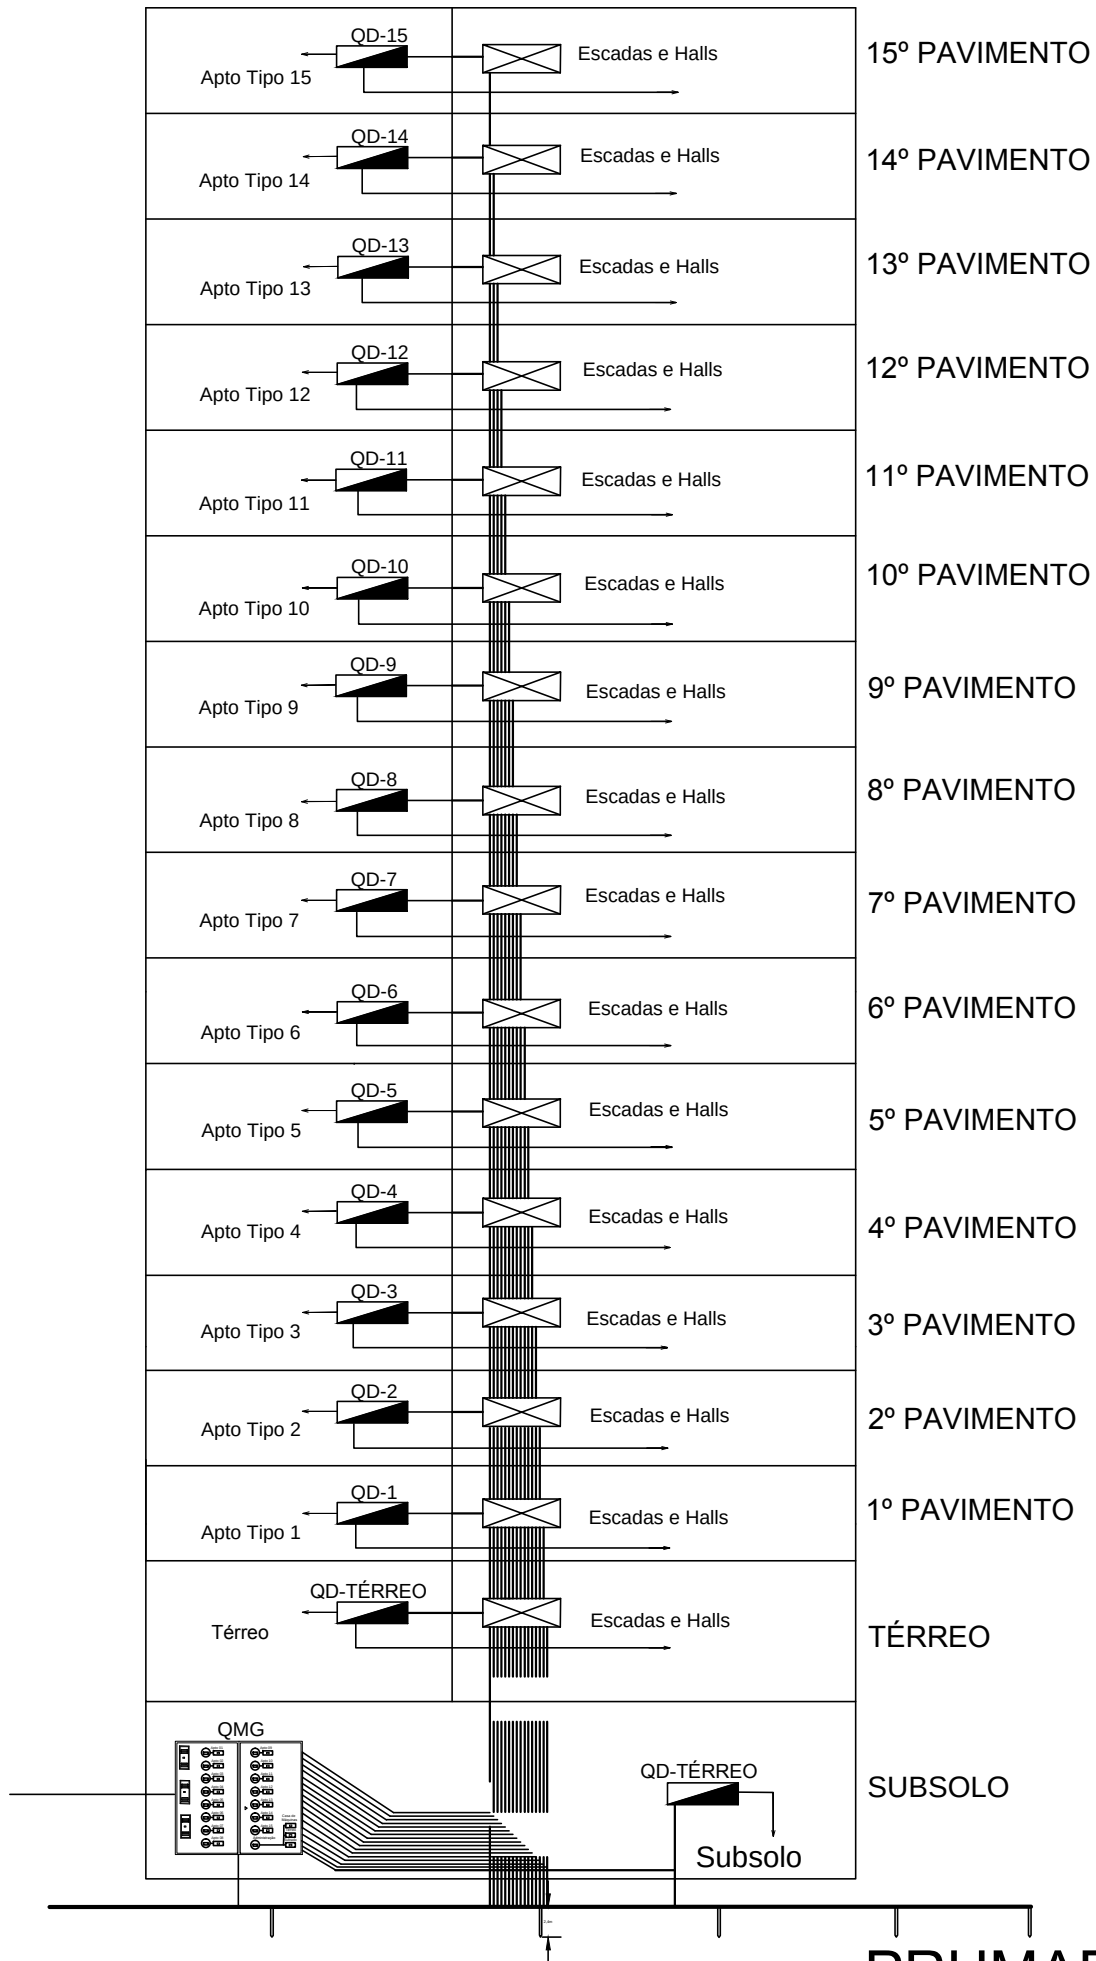
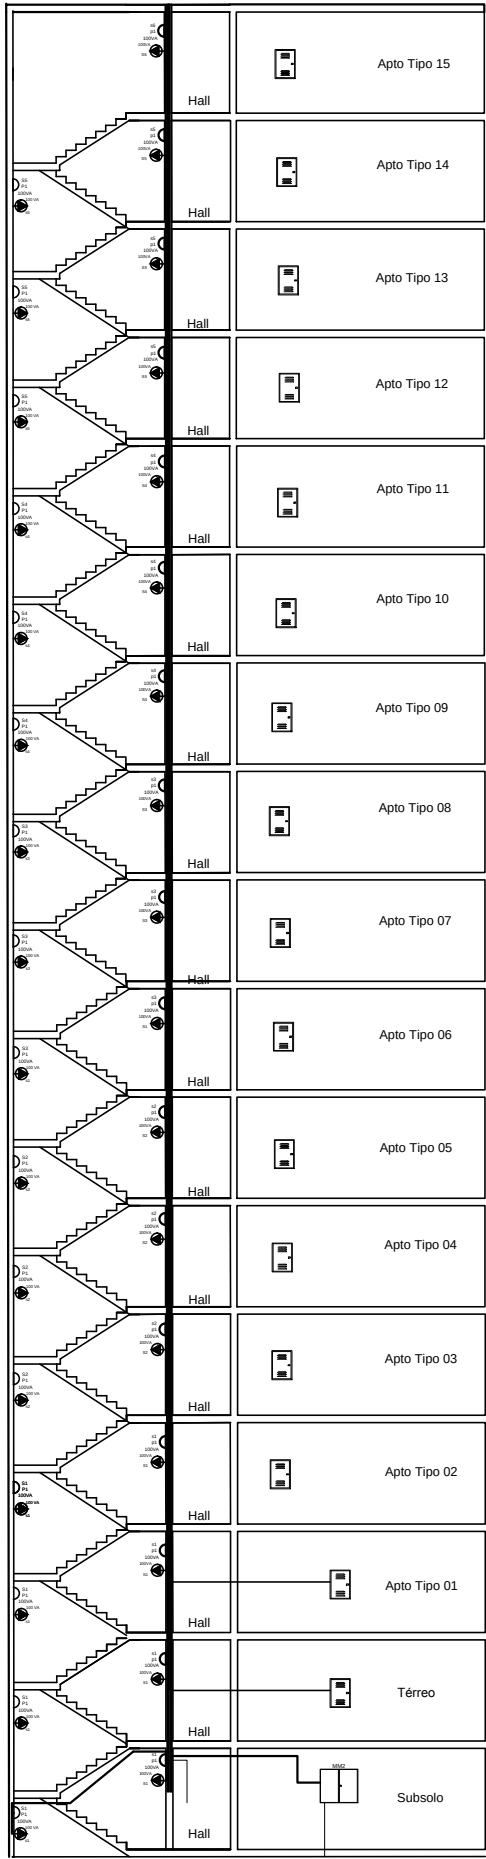


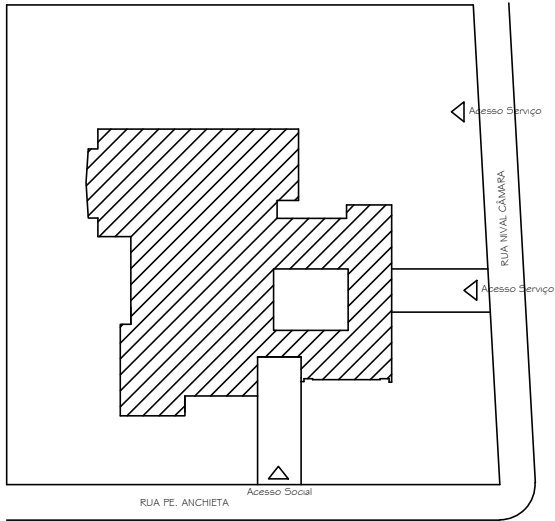

PRUMADA ELÉTRICA
1/50

Escala

Legenda Técnica	
	Caixa de Passagem e Eletrodutos
	Quadro de Distribuição Terminal
	Quadro de Medição Geral
	Dijuntor Geral do Entrada
	Medidores para os Circuitos
	Dijuntor Geral dos Pavimentos

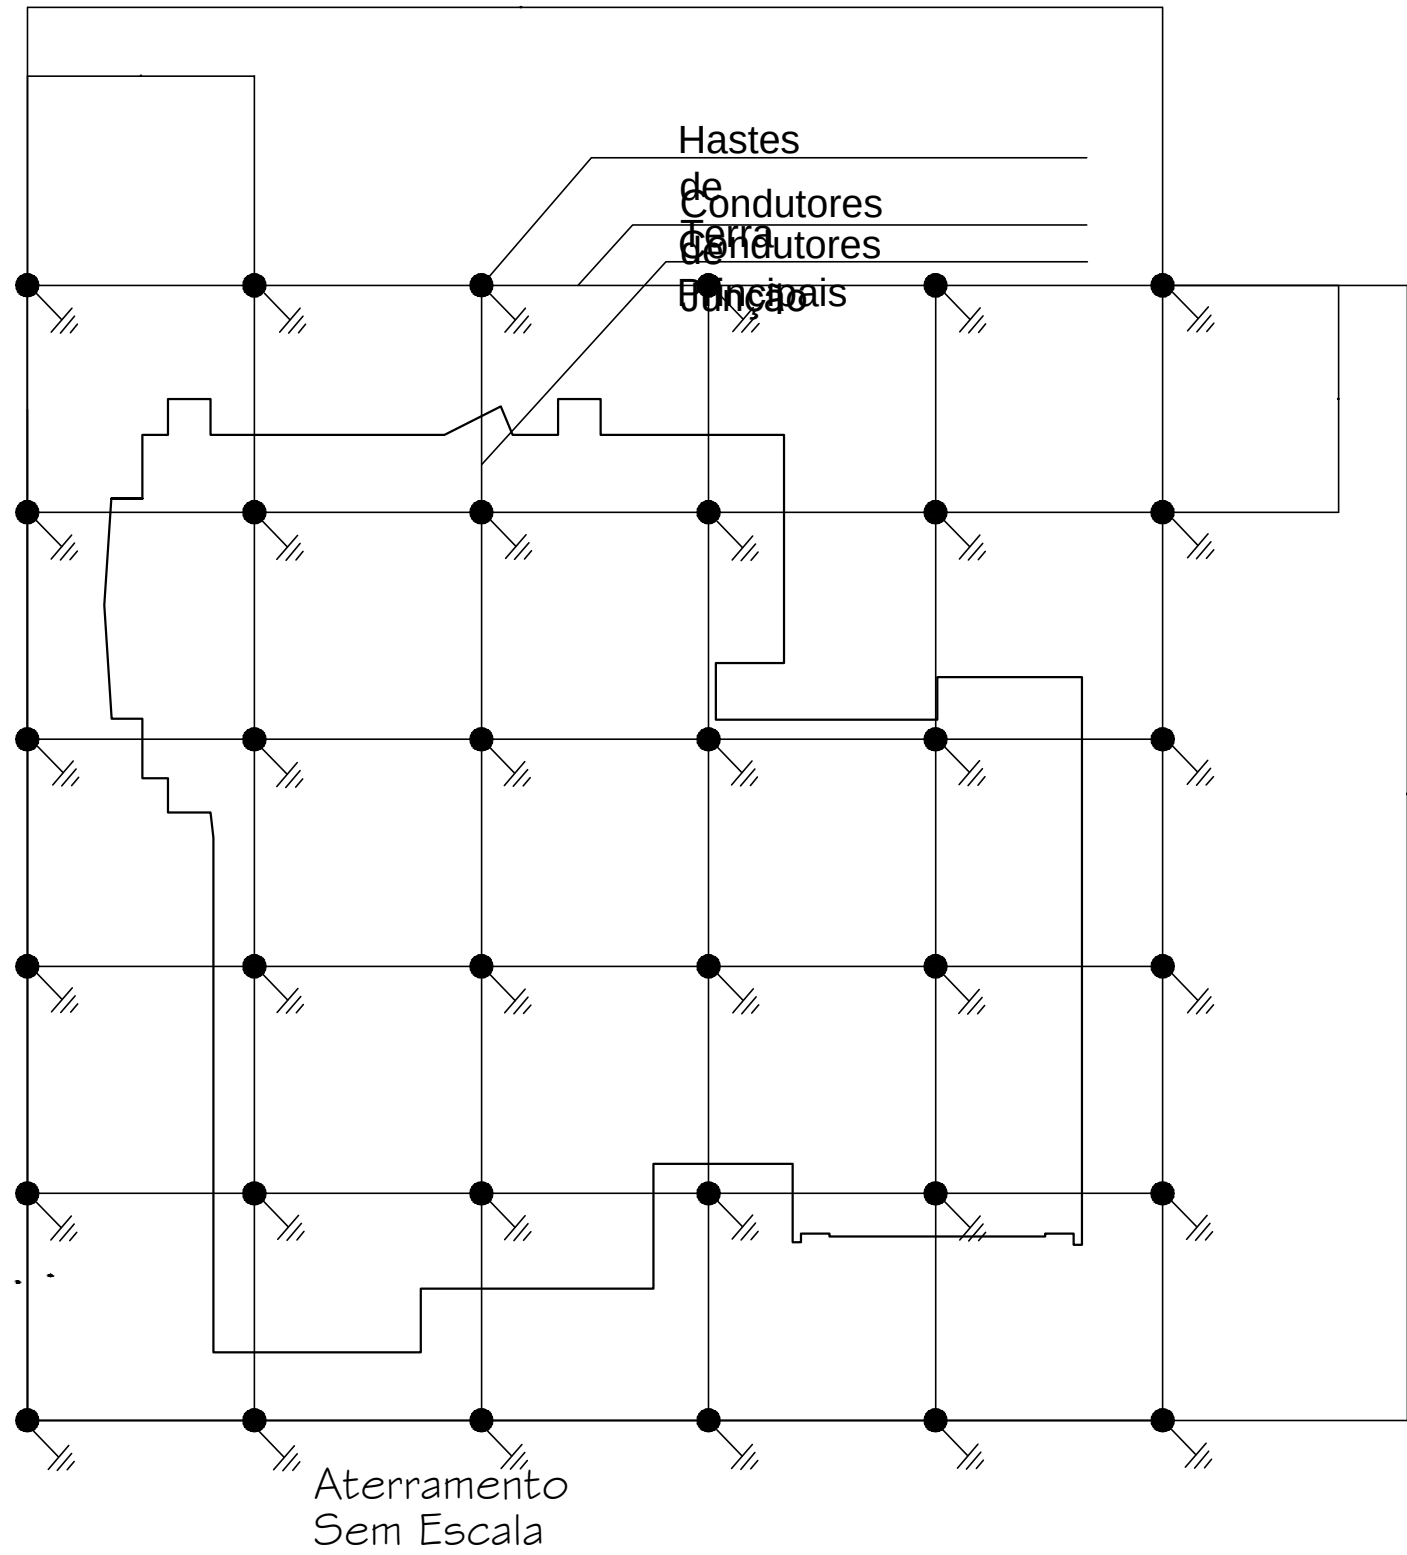

PLANTA DE LOCAÇÃO
Sem Escala

PROJETO DE INSTALAÇÕES ELÉTRICAS UFRN - 2015.1			
CLIENTE:		José Luiz da Silva Júnior	
OBRA:		Projeto de um Edifício Residencial	
Detalhamento do Projeto Elétrico			
PROJETISTAS: Frankelene Pinheiro/ Lucas Marcelino/ Pedro Yochinori		DESENHISTA: Pedro Yochinori	Prancha: 04/04
ESCALA: 1:50	DATA: 03/06/2015	ARQUIVO: Planta_Cortes.dwg	